
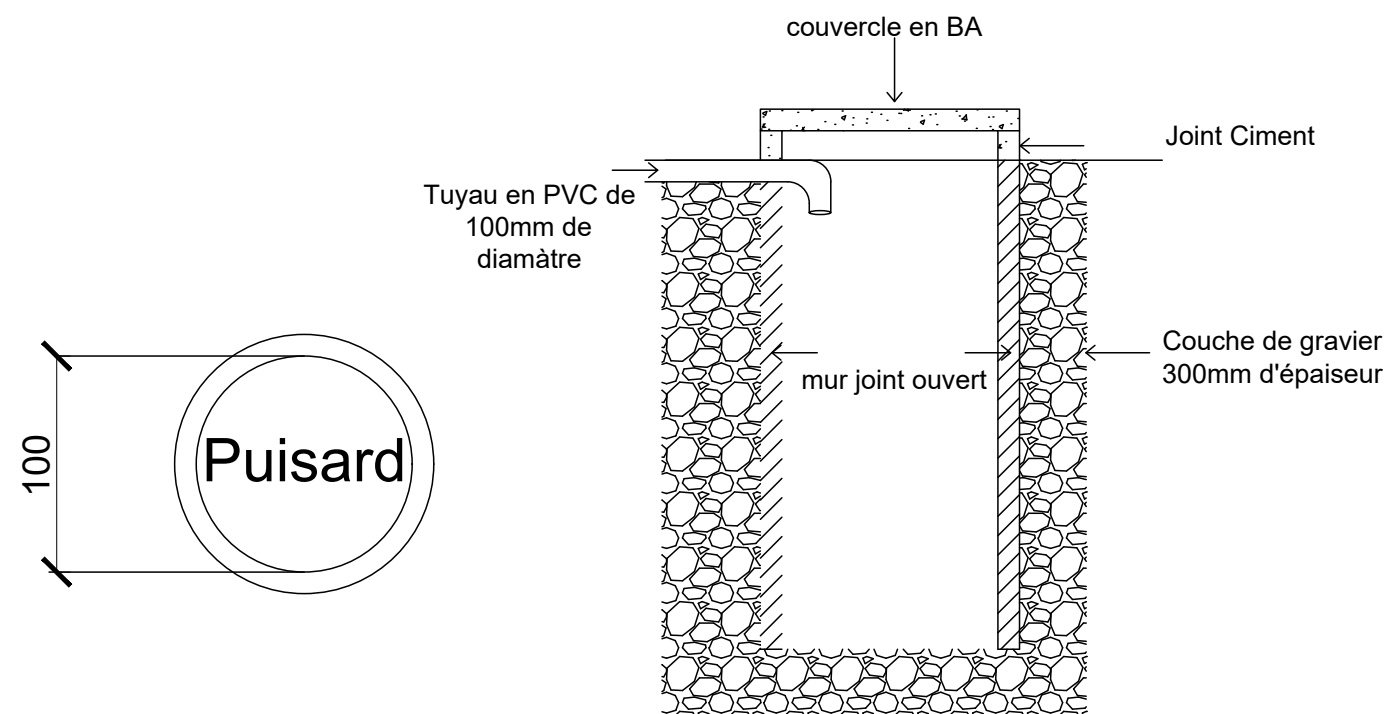


DETAILS DE FOSSE
SEPTIQUE ET PUISARD

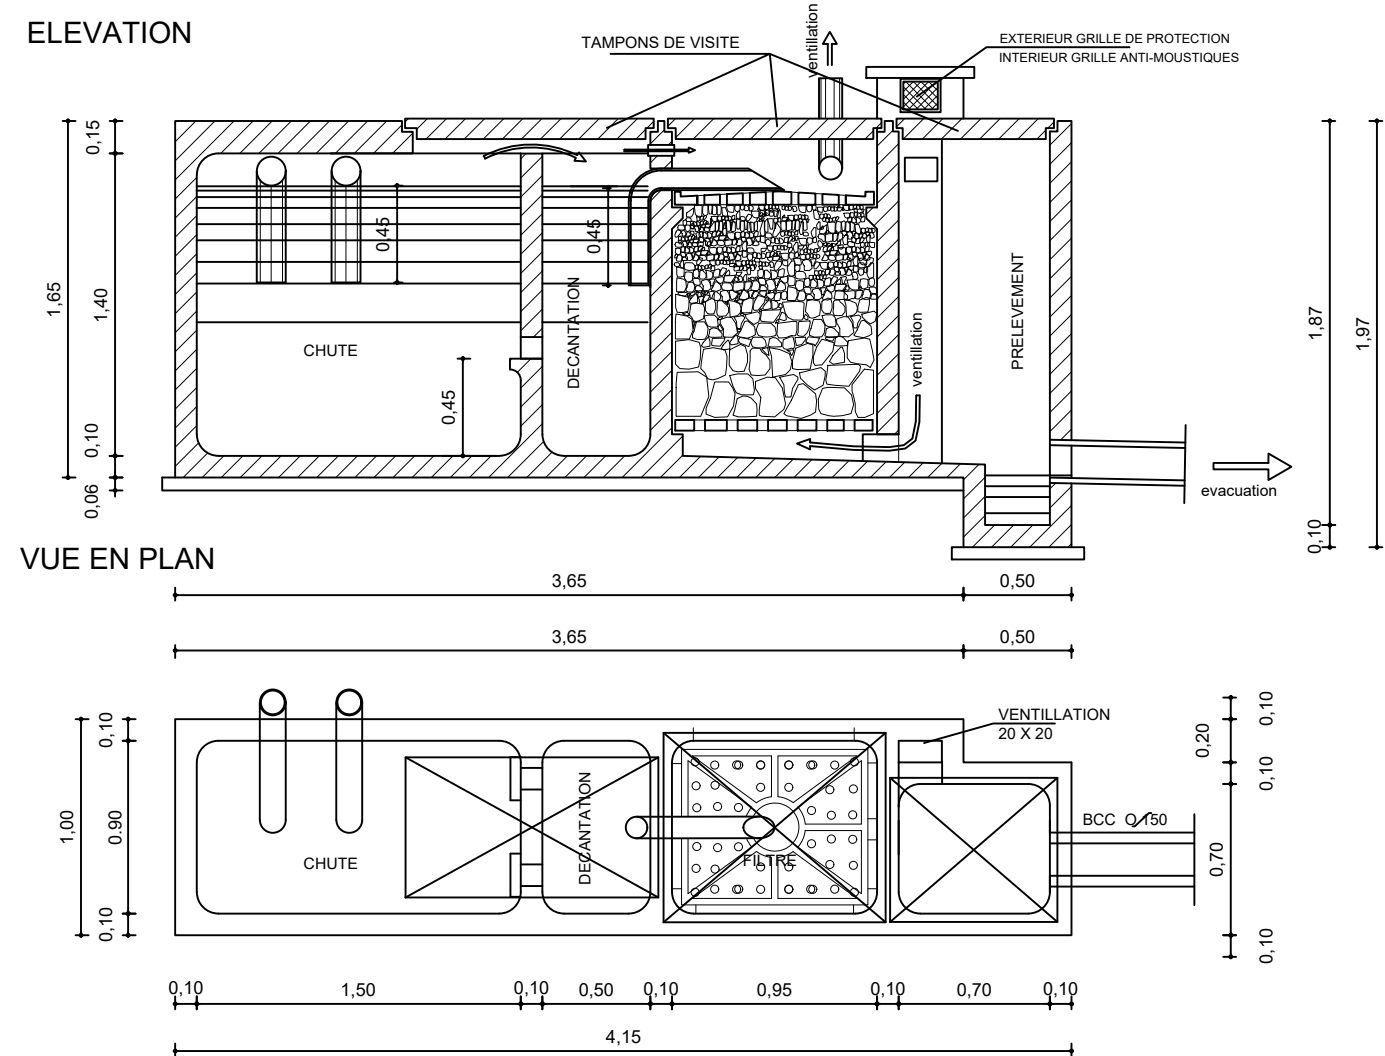

La profondeur dépend du niveau de la couche à capacité d'absorption élevée perméable

Nouvelle construction d'une maison R+2
sise à Fianarantsoa
Fkt Ambatovory

MR RIJANOMENJANAHARY YVES

FOSSE SEPTIQUE ET PUISARD

DATE : 08/09/2025

ECHELLE : 1 / 40(Format A3)



N°15