
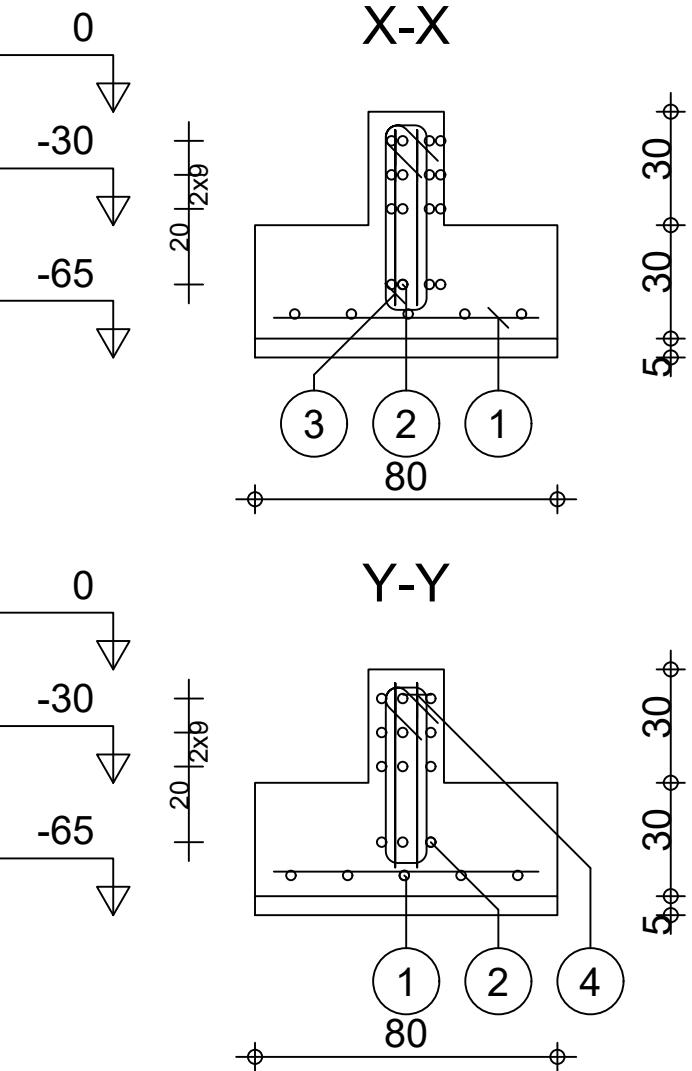


PLAN DE FERRAILLAGE

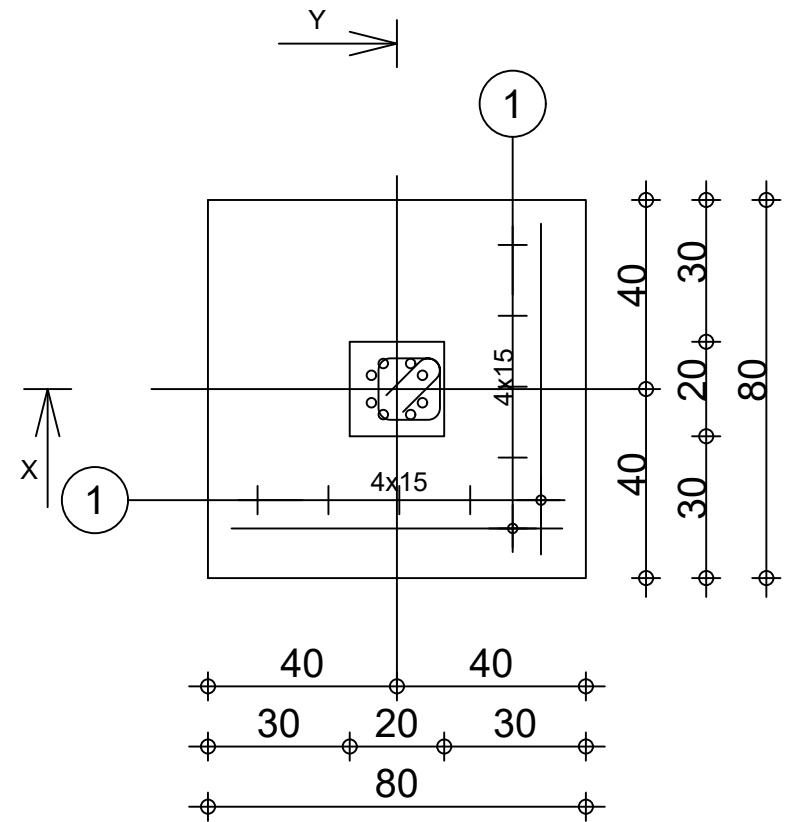

Pos.	Armature	Code	Forme	Pos.	Armature	Code	Forme		
(1)	10HA 10	I=70	00	70	(4)	2HA 12	I=1.48	31	
(2)	4HA 10	I=76	31						
(3)	2HA 12	I=1.43	31						

Nouvelle construction d'une maison R+2
sise à Fianarantsoa
Fkt Ambatovory

MR RIJANOMENJANAHARY YVES

SEMELLE 80x80

DATE : 08/09/2025

ECHELLE : 1 / 16(Format A3)