
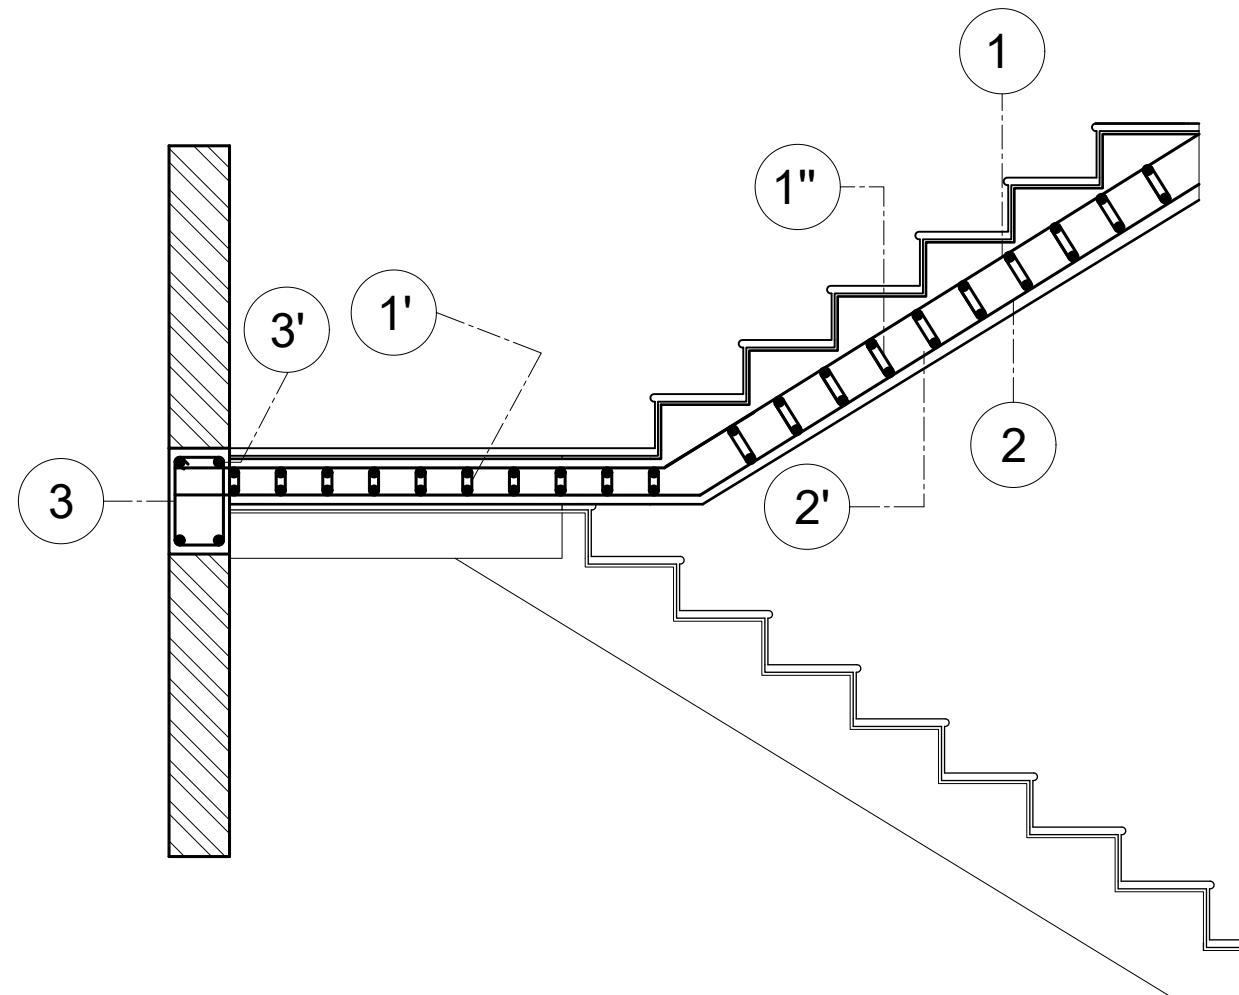


PLAN DE FERRAILLAGE

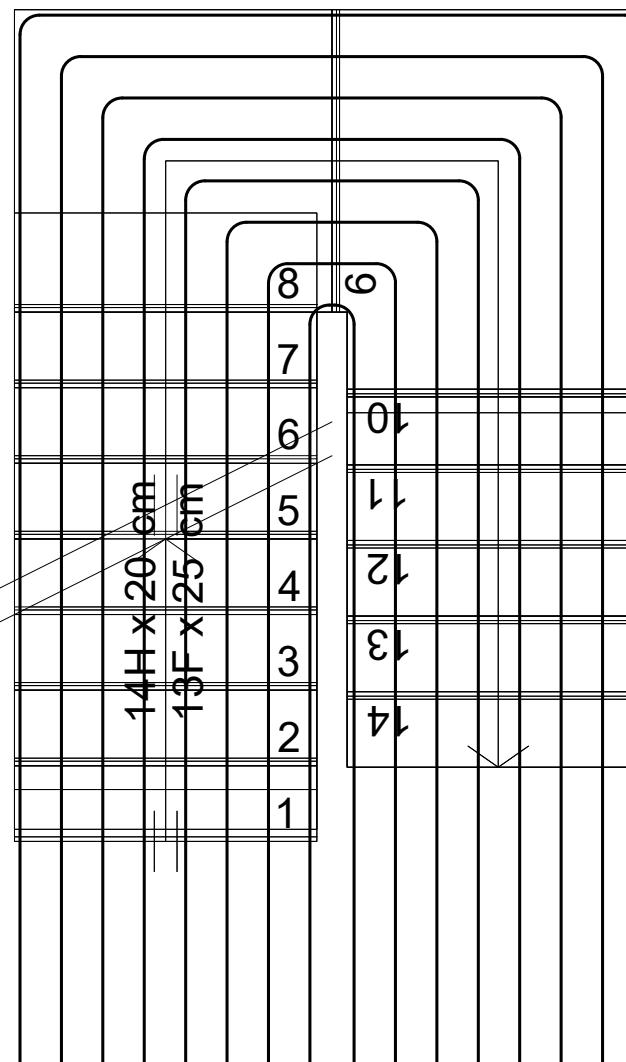

Pos.	Armature	Code	Forme
(1)	8 HA 10 l=8.70_4.50		
(1')	352 HA 8 l=0.33		
(1'')	134 HA 8 l=0.21		
(2)	8 HA 10 l=8.70_4.50		
(2'')	133 HA 10 l=1.05		
(3)	16 HA 6 l=1.12		
(3'')	4 HA 10 l=2.45		

Nouvelle construction d'une maison R+2
sise à Fianarantsoa
Fkt Ambatovory

MR RIJANOMENJAHARY YVES

ESCALIER

DATE : 08/09/2025

ECHELLE : 1 / 25(Format A3)