
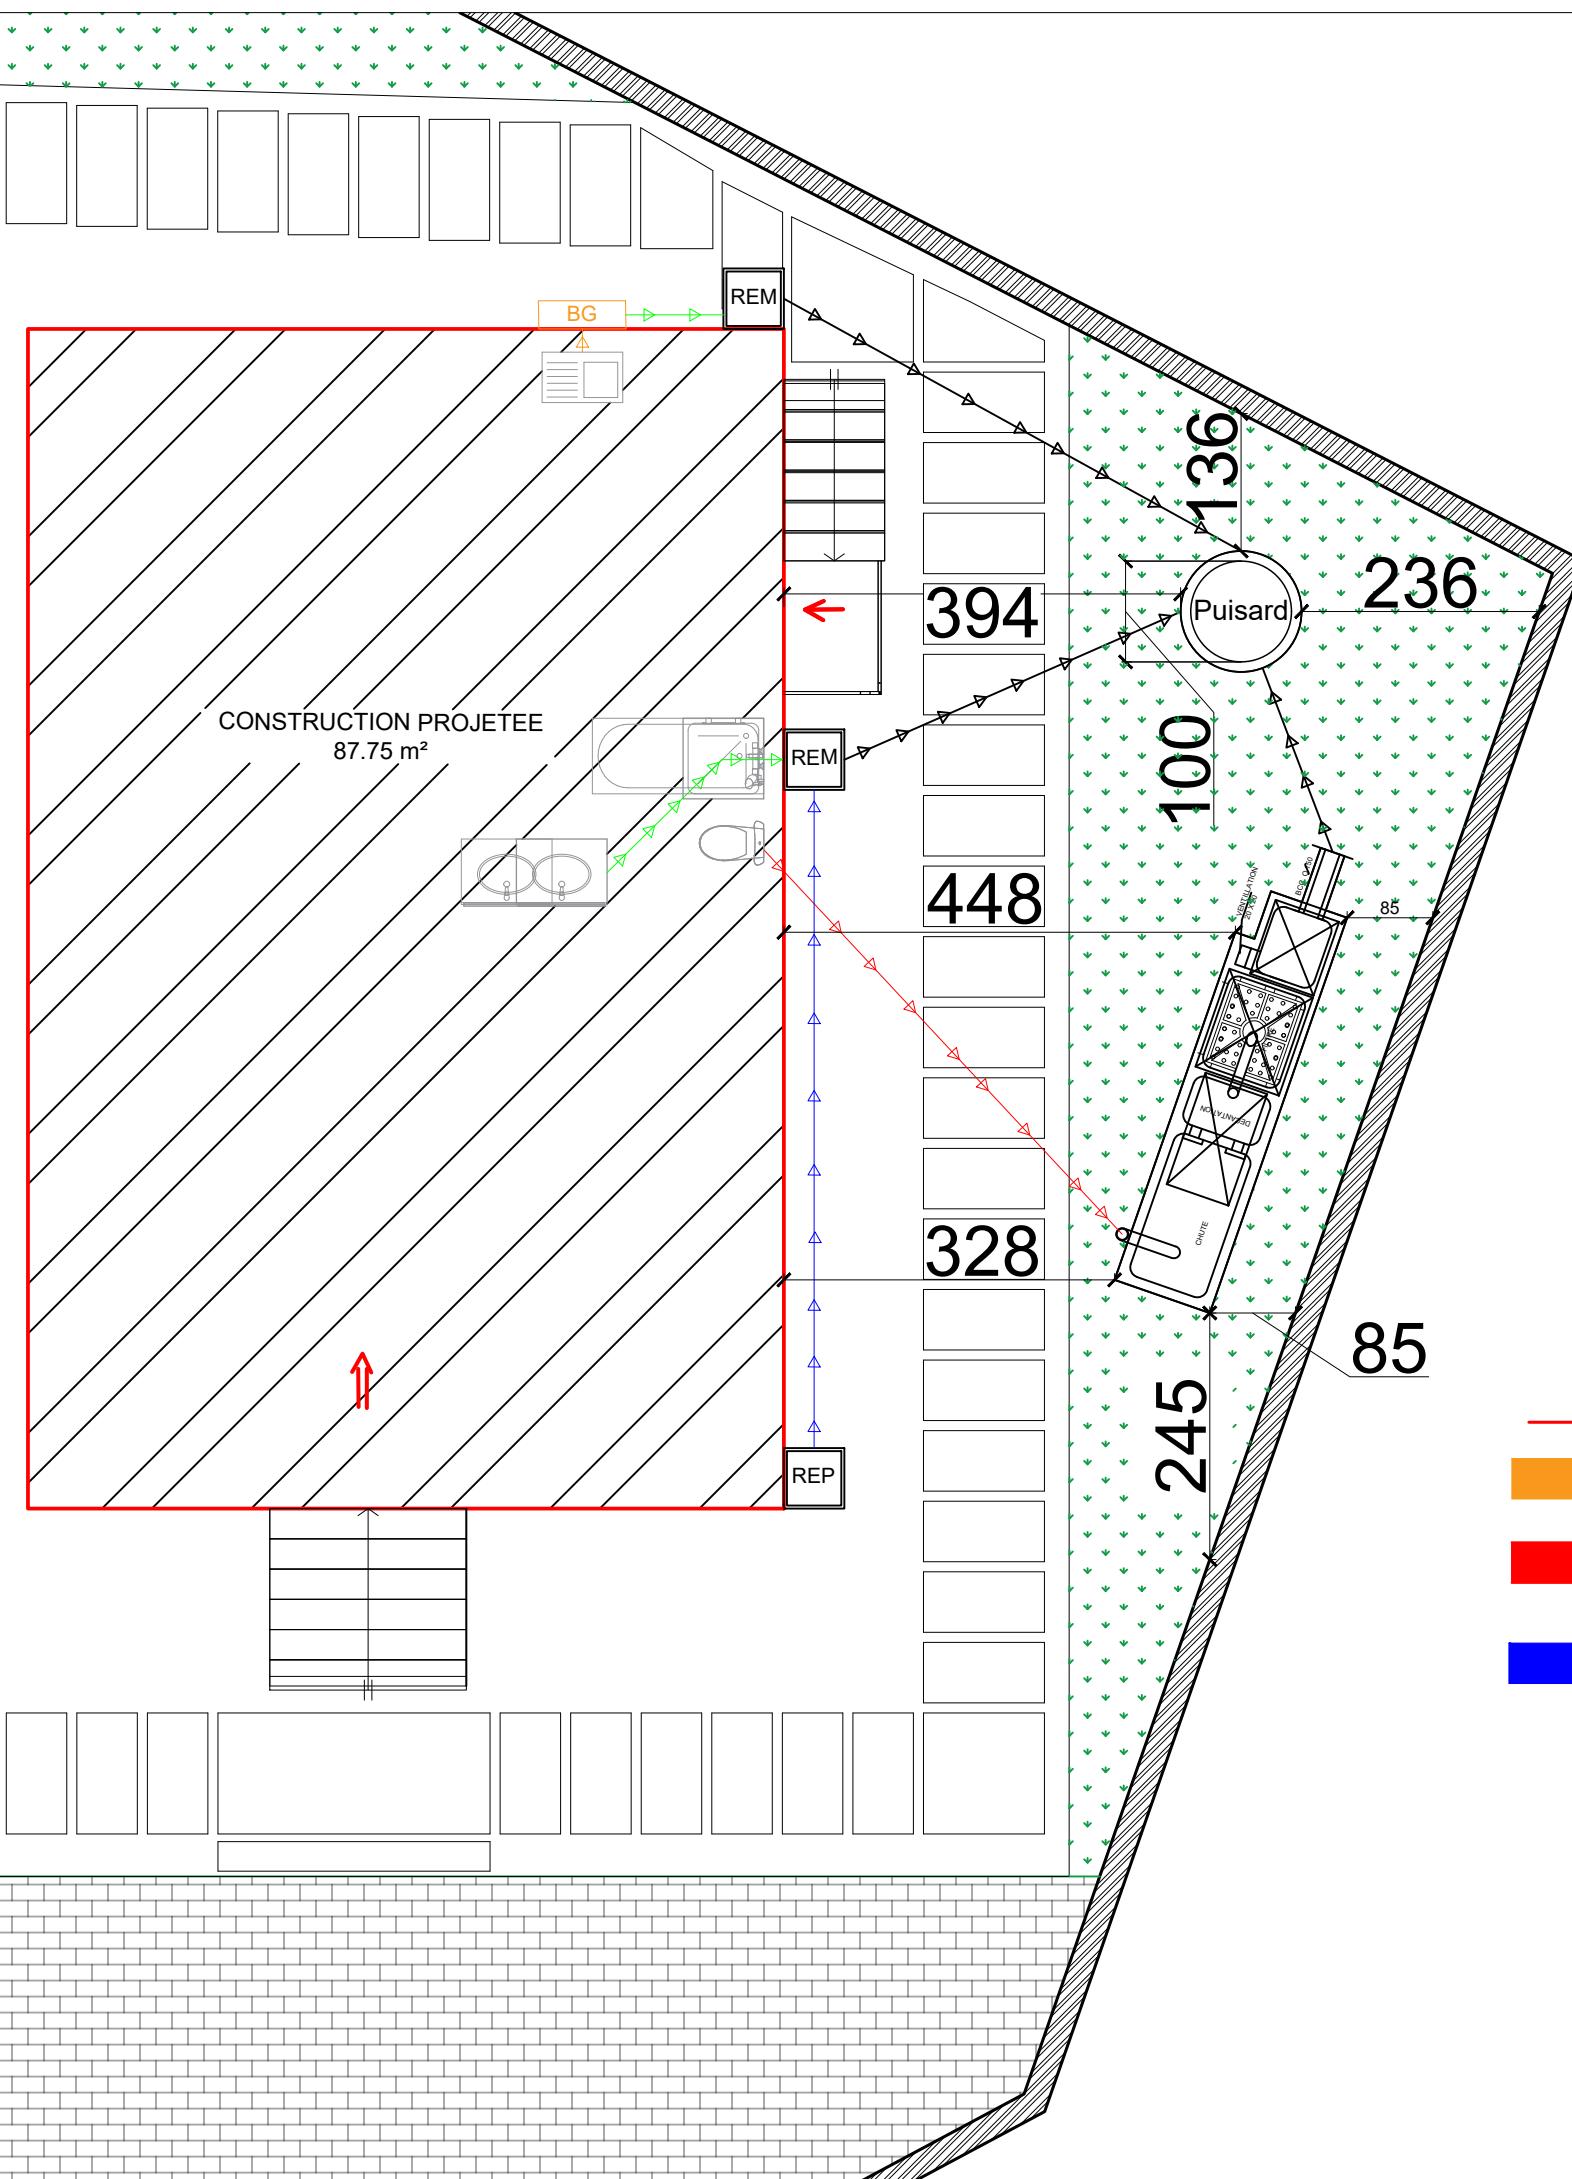


PLAN D'ASSAINISSEMENT

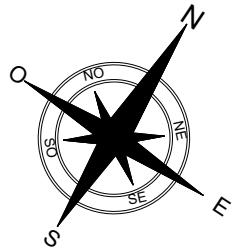

- [Green pattern] Espace vert
- [Hatched pattern] Limite de la propriété
- [Red line] Construction projetée
- [Orange bar] Eau usée
- [Red bar] Eau vanne
- [Blue bar] Eau pluviale
- [BG icon] Bac à graisse
- [REP icon] Regard eau pluviale
- [REM icon] Regard mixte

Nouvelle construction d'une maison R+2
sise à Fianarantsoa
Fkt Ambatovory

MR RIJANOMENJAHARY YVES

ASSAINISSEMENT

DATE : 08/09/2025

ECHELLE : 1 / 75(Format A3)